


会签栏 CONFIRMATION

专业	签字	日期	专业	签字	日期

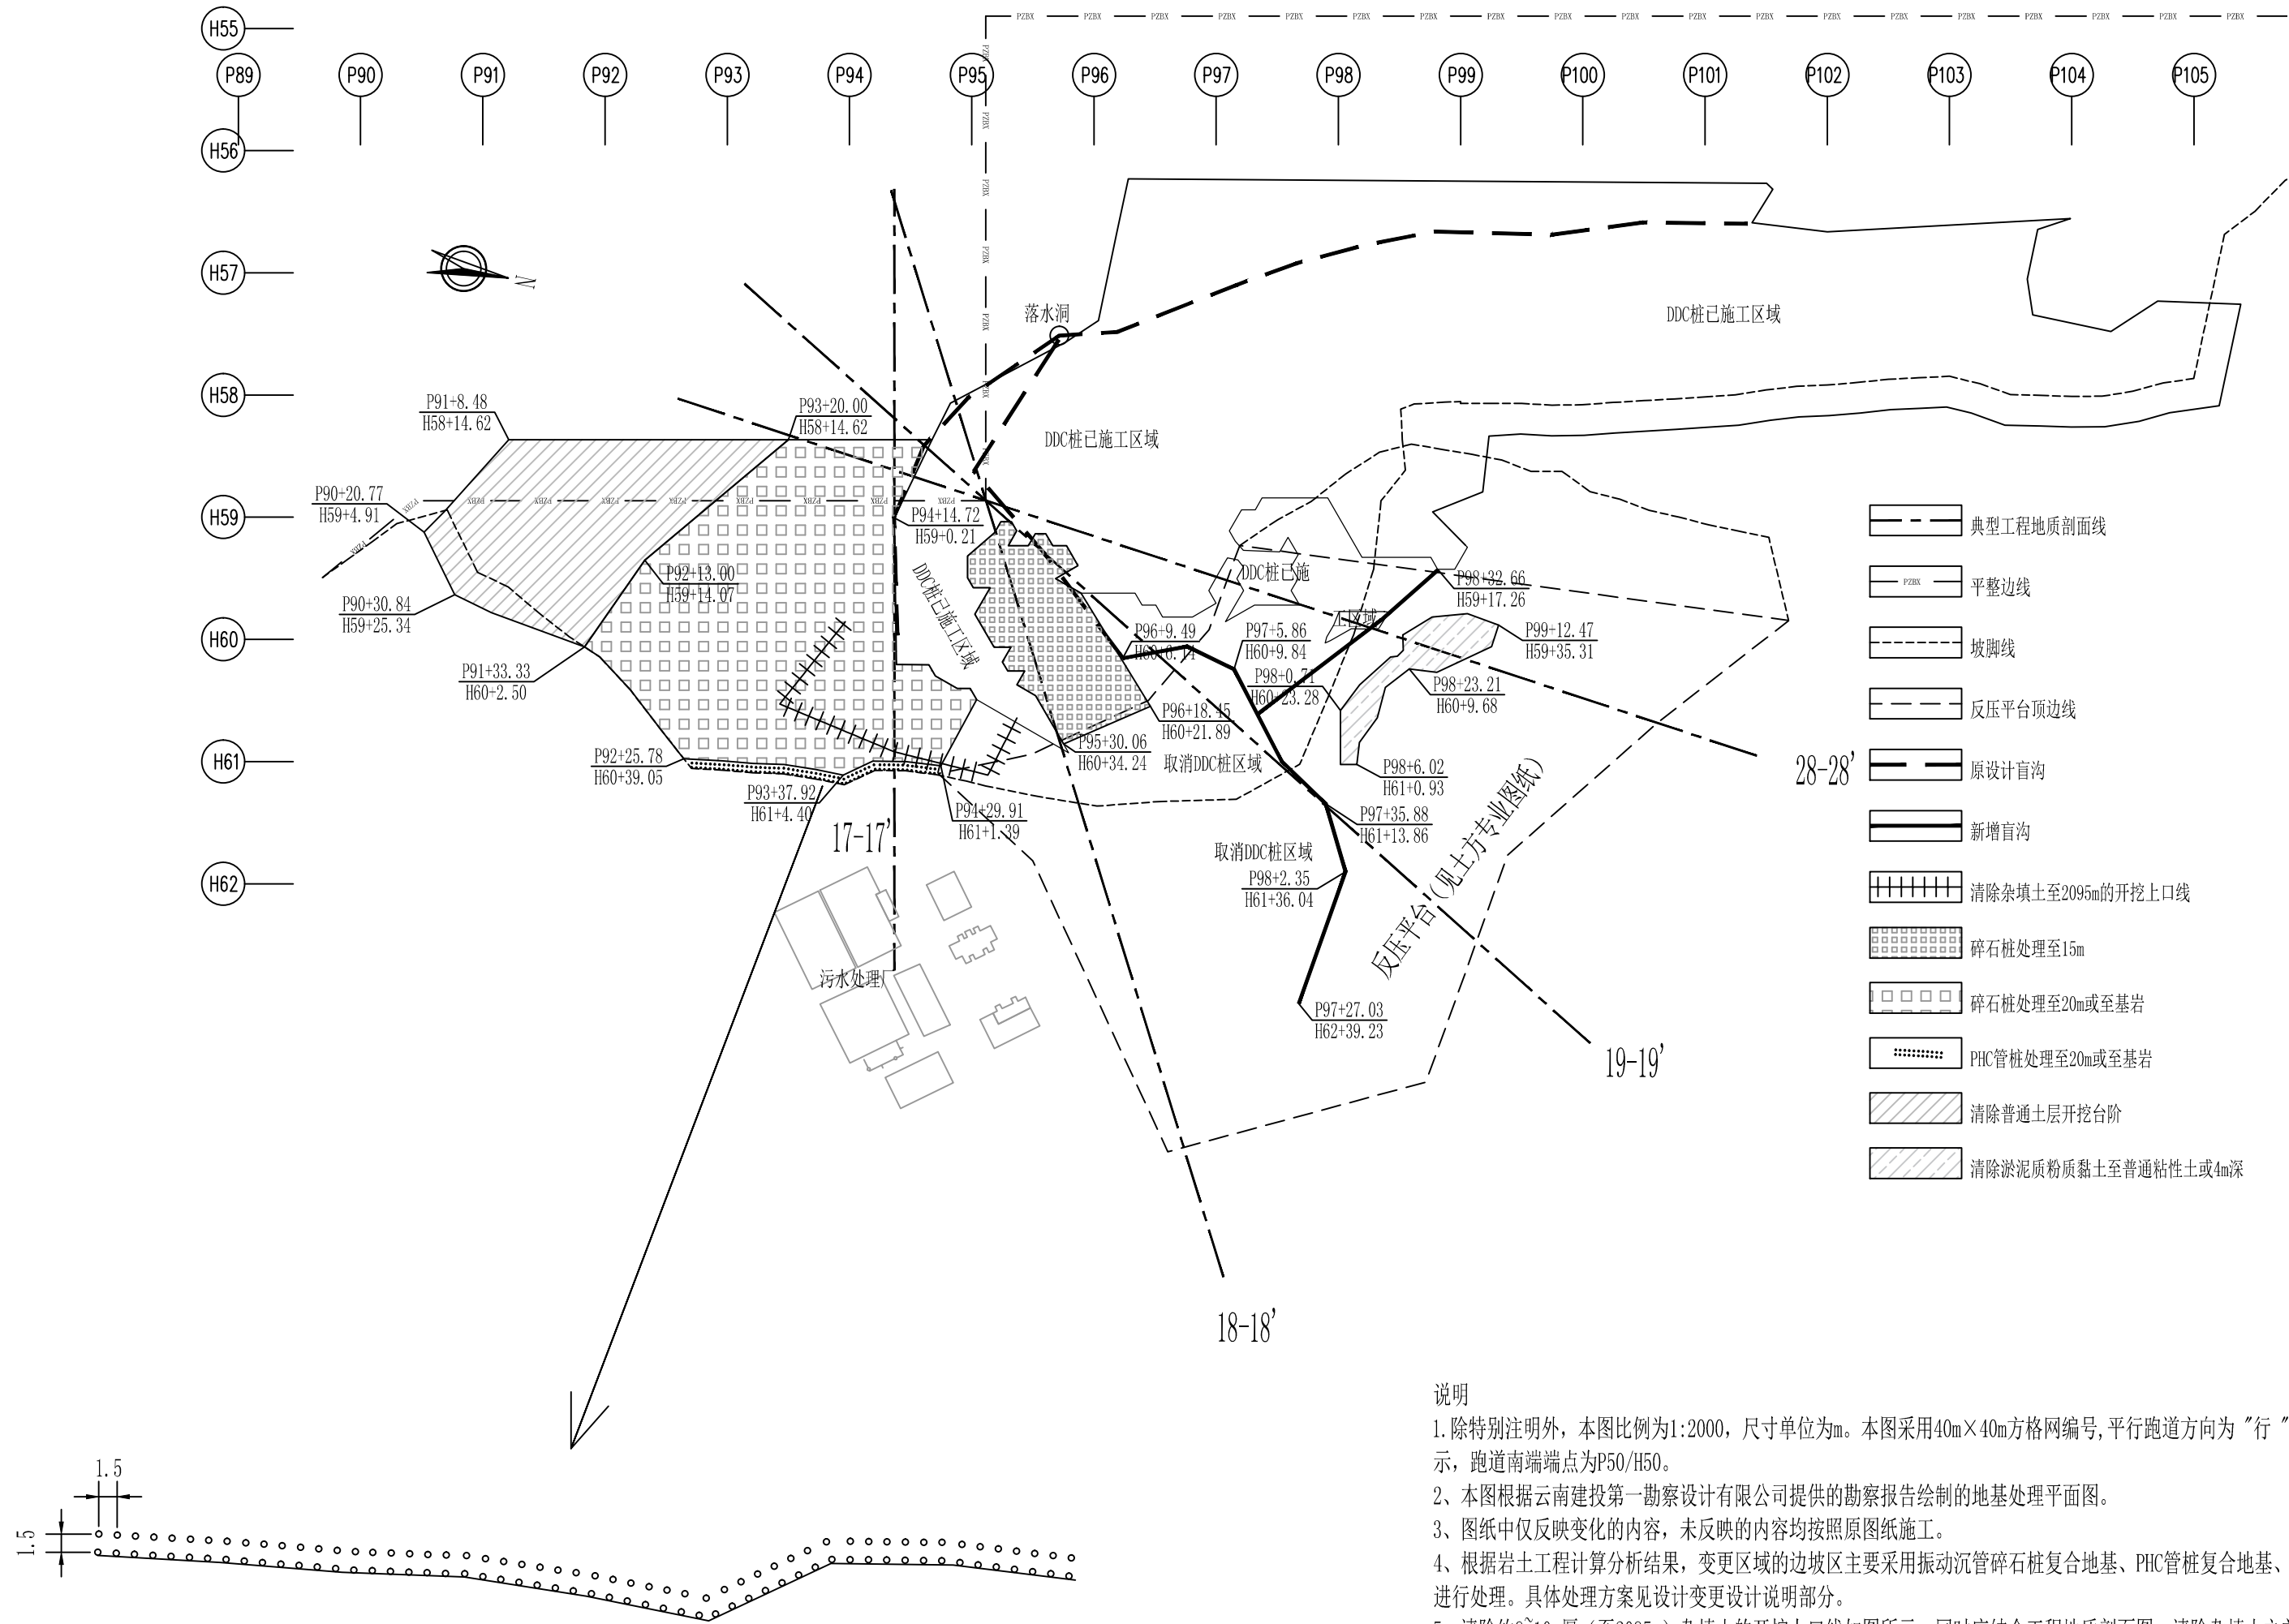

PHC管桩桩位布置平面图

平面定位图

说明

- 除特别注明外，本图比例为1:2000，尺寸单位为m。本图采用40m×40m方格网编号，平行跑道方向为“行”，用“H”表示，垂直跑道方向为“排”，用“P”表示，跑道南端端点为P50/H50。
- 本图根据云南建投第一勘察设计有限公司提供的勘察报告绘制的地基处理平面图。
- 图纸中仅反映变化的内容，未反映的内容均按照原图纸施工。
- 根据岩土工程计算分析结果，变更区域的边坡区主要采用振动沉管碎石桩复合地基、PHC管桩复合地基、清除杂填土、开挖台阶、设置反压平台等方式进行处理。具体处理方案见设计变更设计说明部分。
- 清除约9~10m厚（至2095m）杂填土的开挖上口线如图所示，同时应结合工程地质剖面图。清除杂填土之前，应迁改坡脚线内及其附近的市政排水涵，清除杂填土的开挖坡比为1:3，施工单位应编制施工专项方案，应先填筑到该区域标高后再分块开挖，处理完成后尽快进行石方填筑，施工过程中做好临时边坡防护措施。
- 延长原设计的一条盲沟和新增一条盲沟，盲沟平面走向可根据现场实际地形进行调整；盲沟底面坡度应根据现场实际情况确定以满足排水需要且不小于0.3%，其它要求见场基施II-05。

工程设计出图专用章
民航机场建设集团西南设计研究院有限公司
证书编号 A15102981 证书分类 民航行业工程设计 资质等级 甲 级
A25102988 建筑工程设计 乙 级
有效期至: 2028年06月07日

设计单位
DESIGN ORGANIZATION



民航机场建设集团西南设计研究院有限公司
CAGC SOUTHWEST DESIGN AND RESEARCH INSTITUTE CO., LTD

民航专业工程施工图审查专用章

单位名称 中国电子工程设计院股份有限公司

证书编号 证书分类 资质等级

A111000405 工程设计 综合甲级

项目名称
PROJECT TITLE

大理机场三期改扩建项目
(飞行区及附属配套工程)

工程名称
ITEM TITLE

场道工程

职 责 FUNCTION	姓 名 NAME	签 字 SIGNATURE
审定人 APPROVED BY	邱存家	邱存家
审核人 REVIEWED BY	王双	王双
专业负责人 DISCIPLINE CHIEF	黄金	黄金
校核人 CHECKED BY	王顶宇	王顶宇
设计人 DESIGNED BY	黄金	黄金

图名
DRAWING TITLE

地基和边坡处理平面图

设计号 PROJECT NO.	2023-0203
图号 DRAWING NO.	场基施II-02 (2/2) 变更
版本号 VERSION	01
专业 DISCIPLINE	岩土
比例 SCALE	如图
日期 DATE	2026年1月