
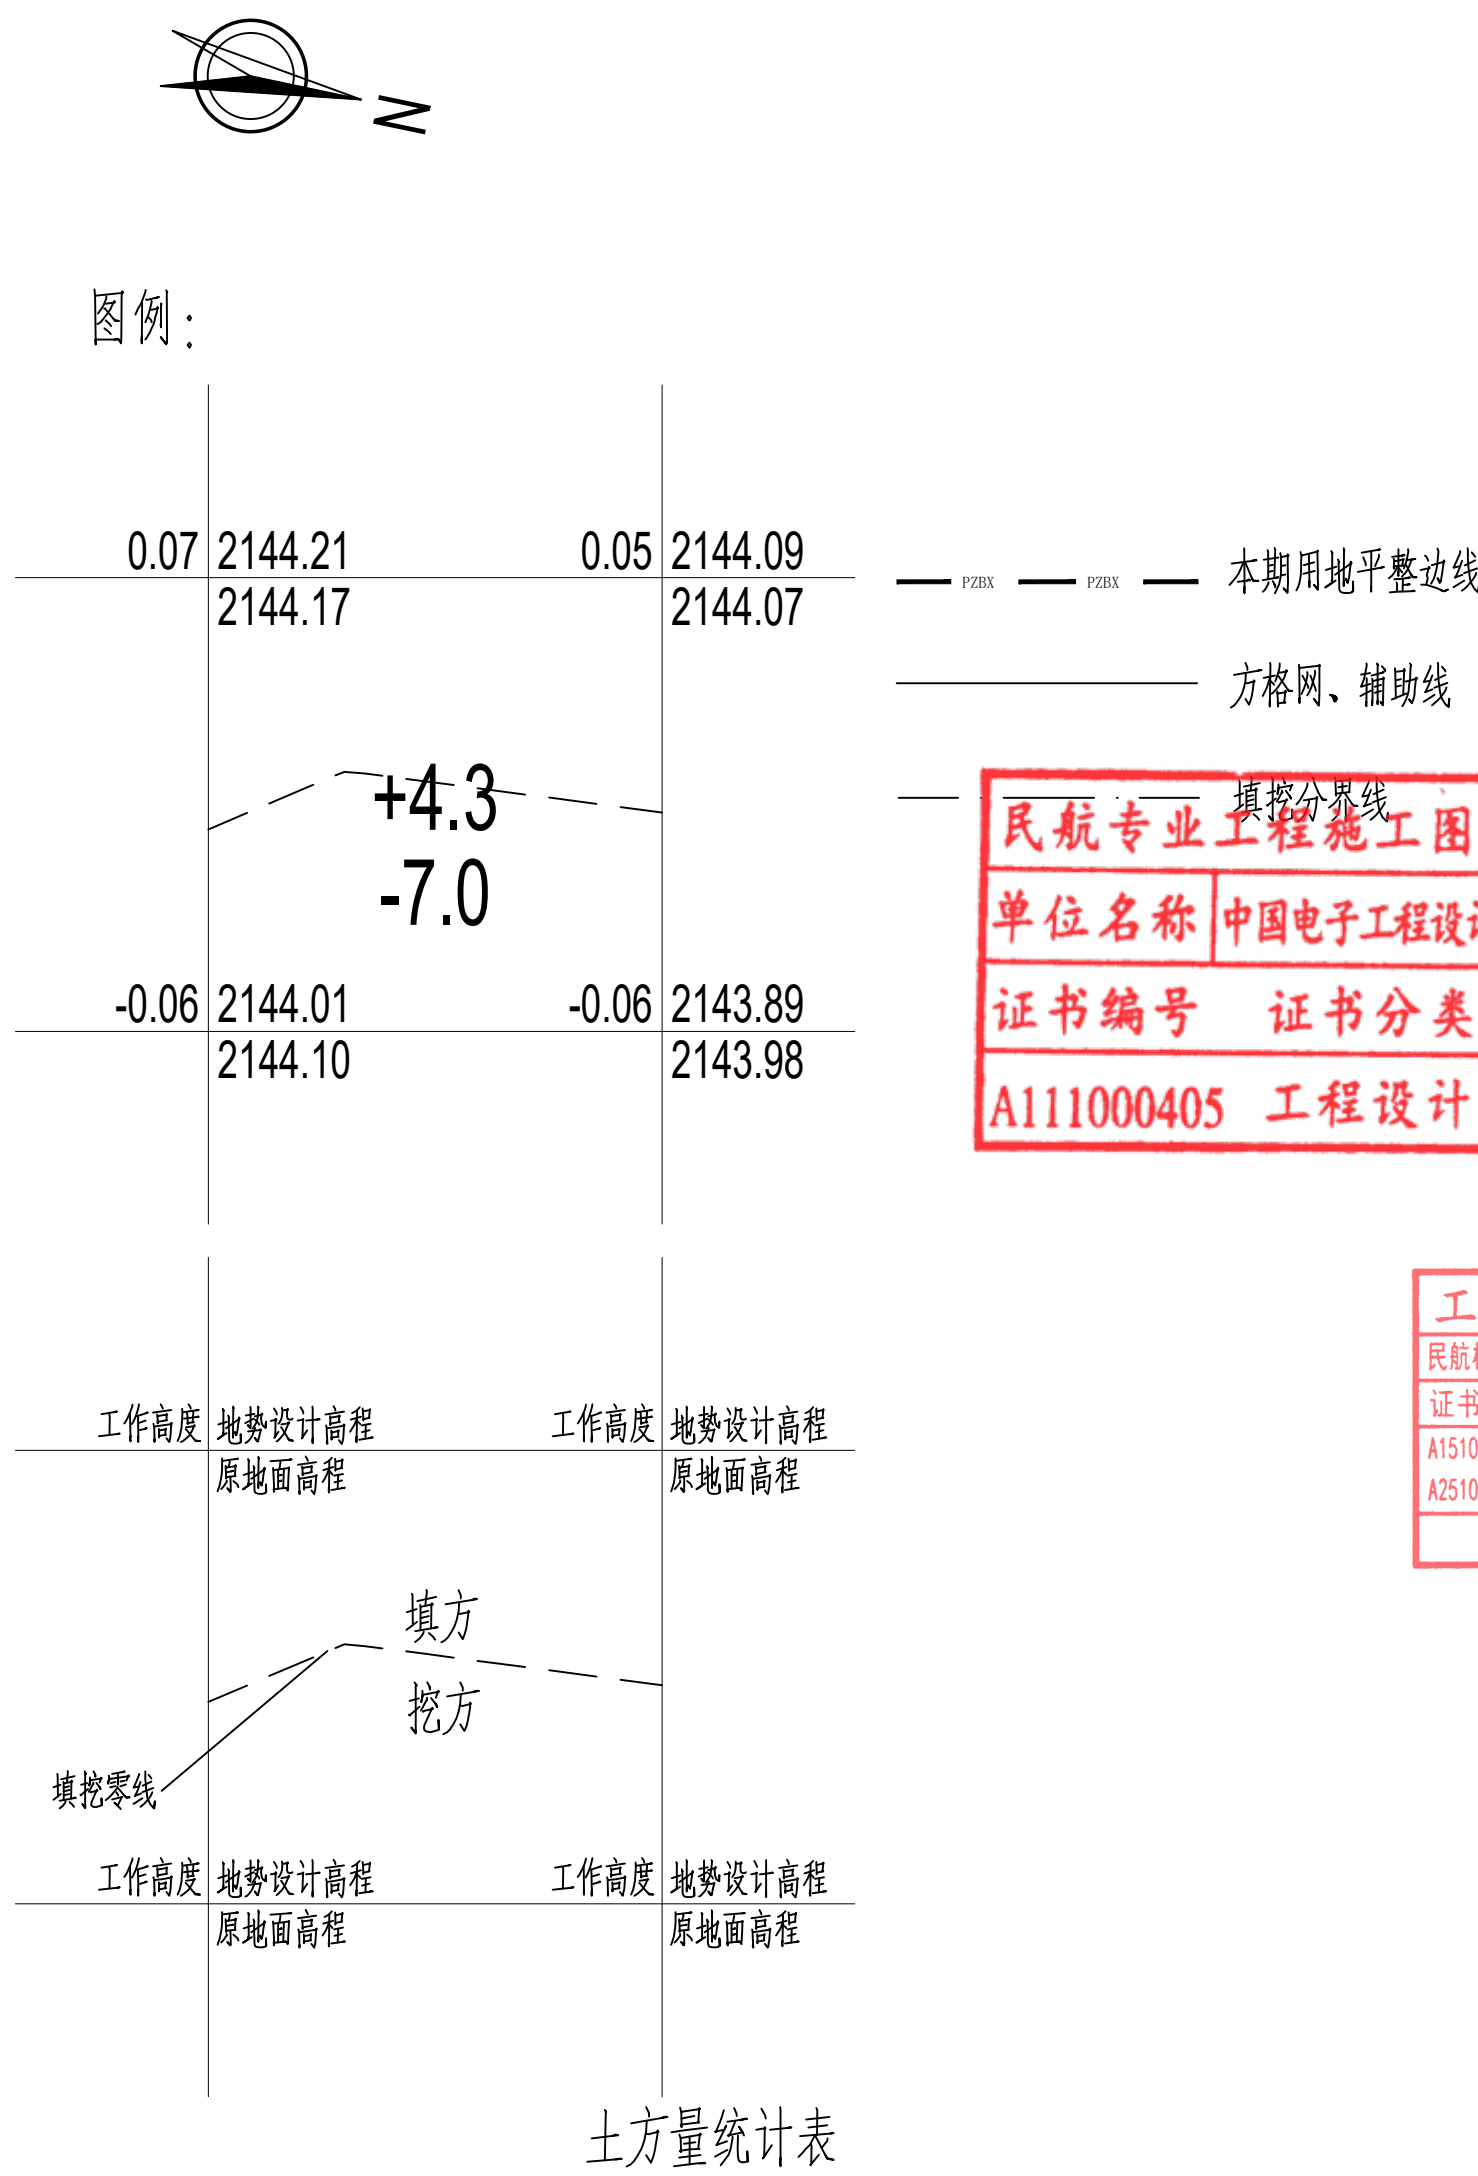


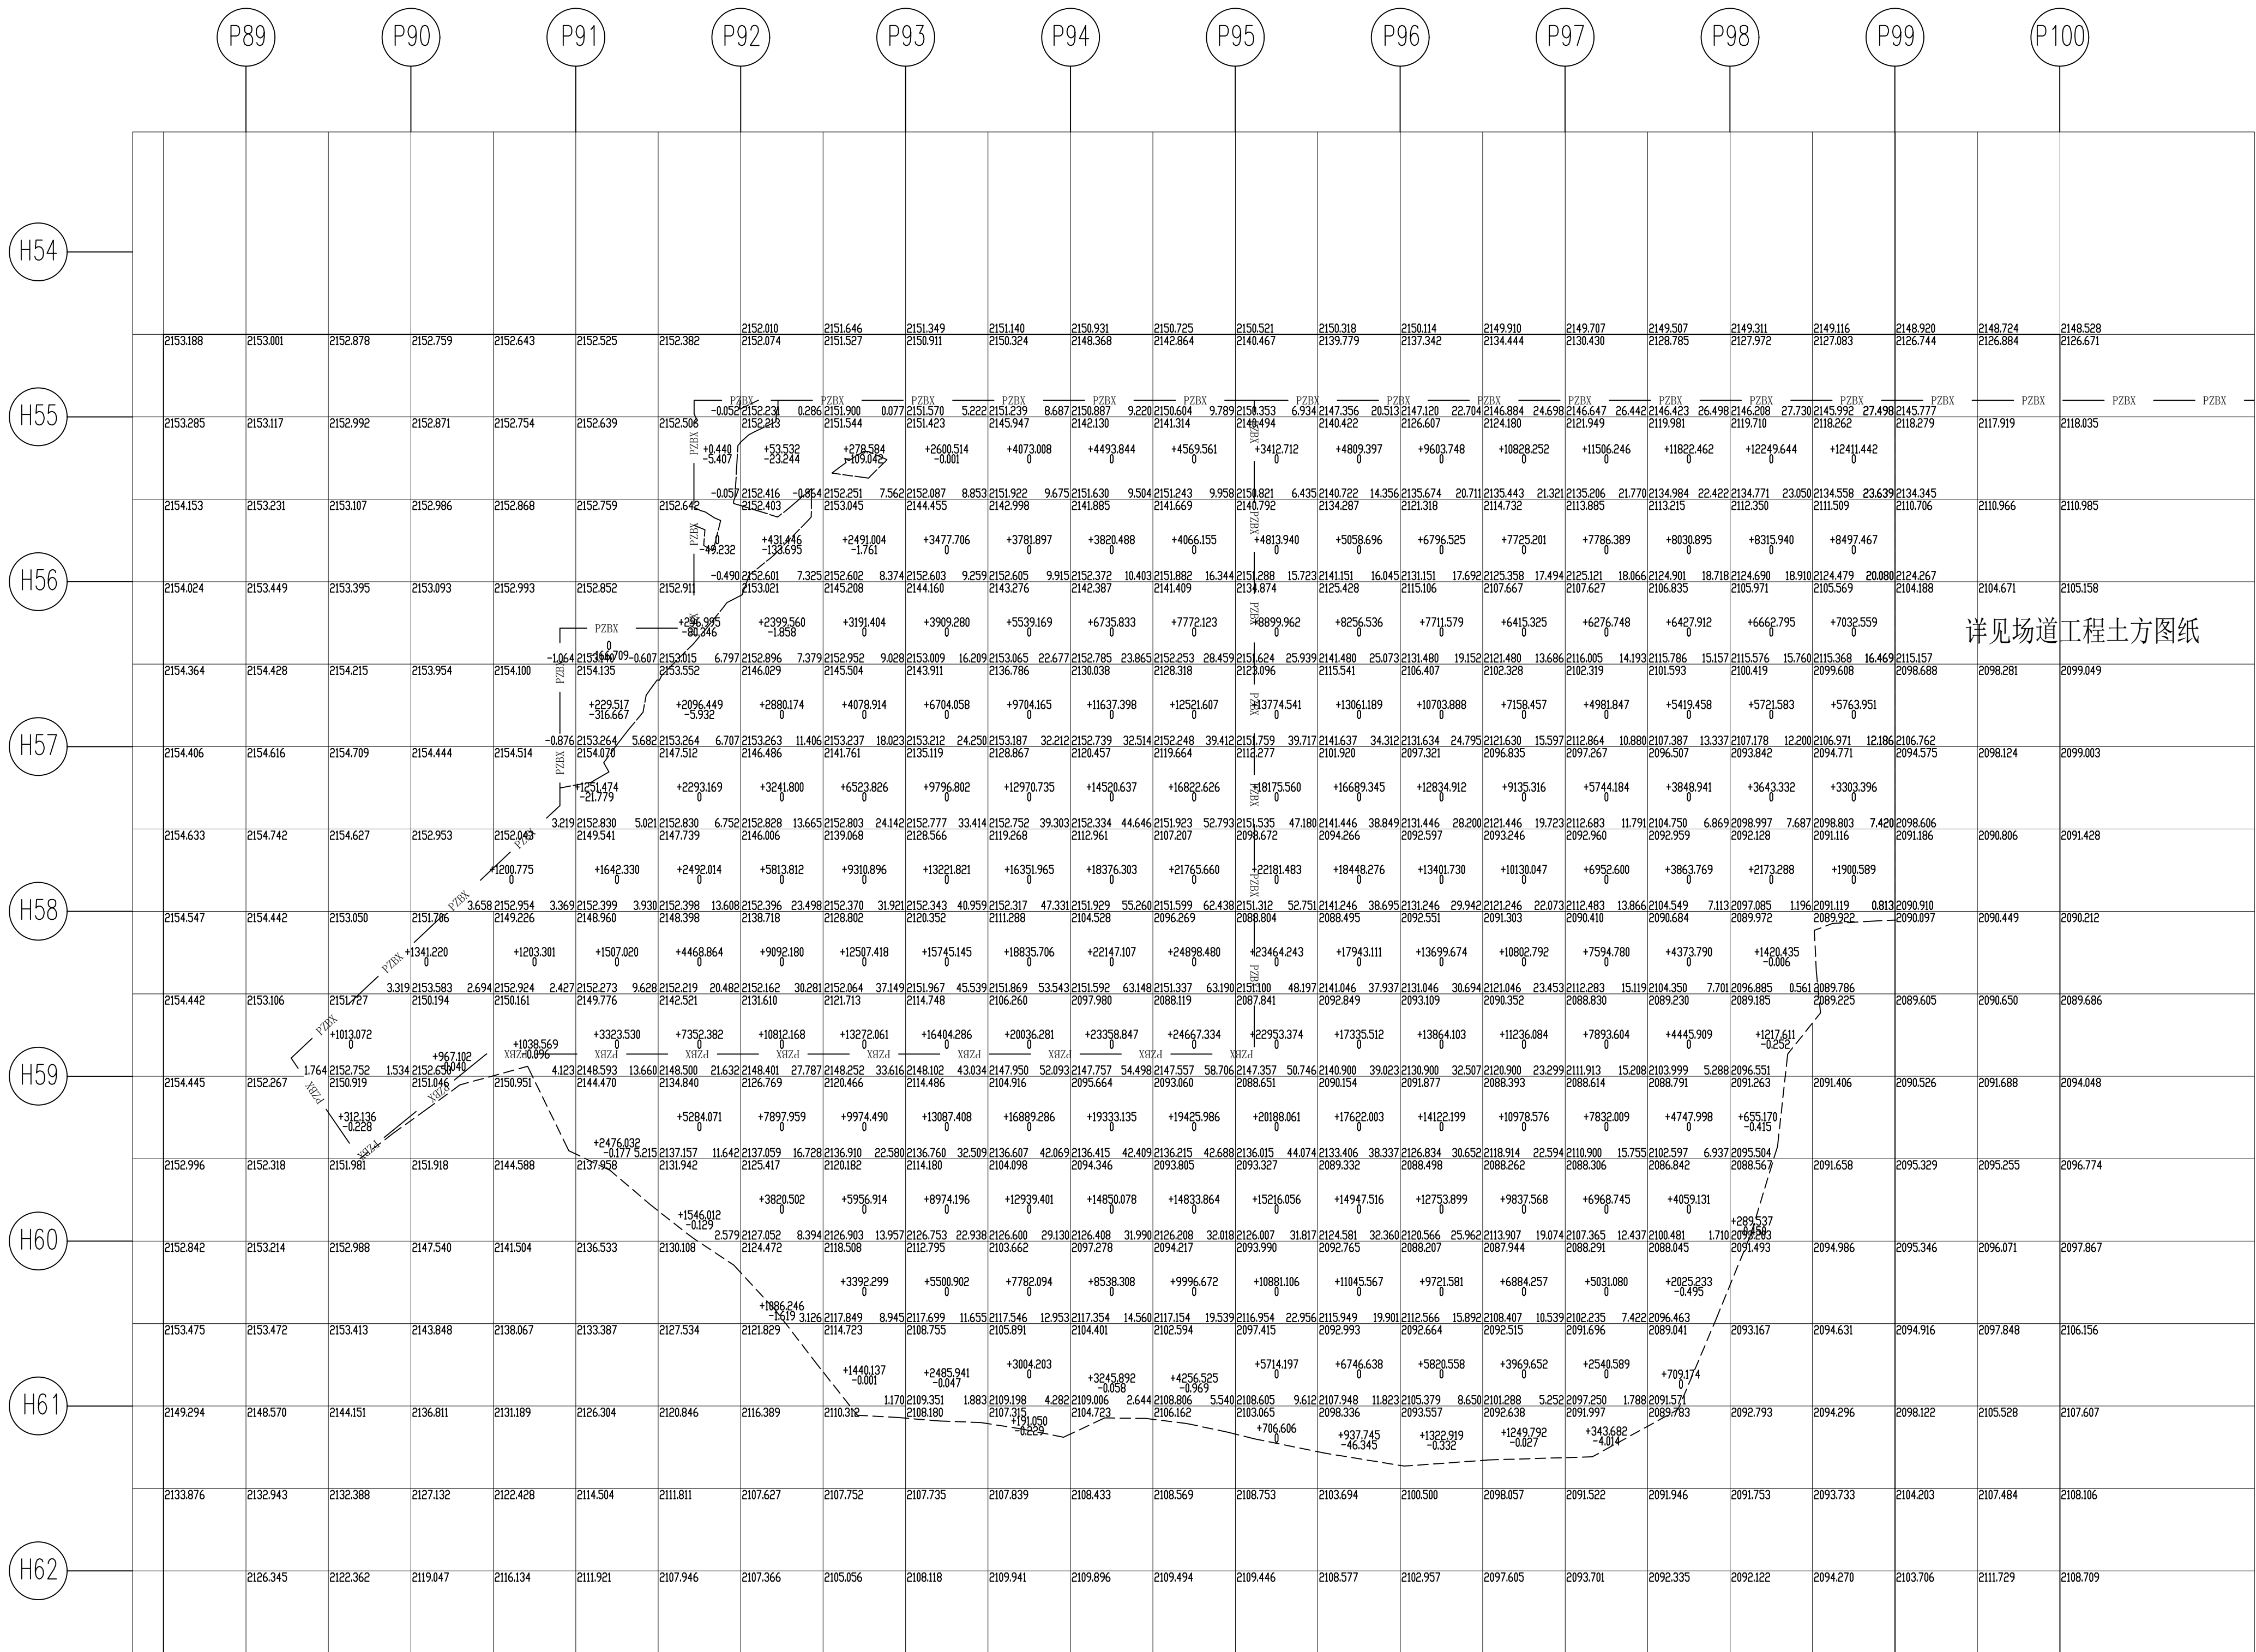

序号	项目	合计
1	图面计算填方量	1497150
2	图面计算挖方量	975
3	填方区挖耕植土面积	27455
4	填方挖耕植土量(0.54m厚)	14818
5	总挖方量	15793
6	总填方量	1497150

注:1、土方量单位为立方米,面积单位为平方米。

说明：

1. 本图使用的地形图包含两部分：机场现状围界范围内及临近区域由中国建筑西南勘察设计研究院有限公司2023年10月提供的测量文件，水塘周边区域根据2025年8月提供的测量文件，尺寸单位以米计。
2. 本图采用机场现有40X40米独立方格网，现跑道南端中点桩号为P50/H50。垂直跑道方向为H坐标，向东递增，平行跑道方向为P坐标，向北递增。
3. 本图中所注高程采用1985年国家高程基准高程。
4. 本次设计范围与现状相接部分，施工时应根据现场实际情况与现有地坪顺接。
5. 土方量采用TDM法进行计算，土方压实标准及范围见地基处理相关要求。
6. 本图所示的土方计算图为该区域边坡填筑，挖方坡比为1:2（每10m高设置一级马道，马道宽2m），填方坡比为1:1.5、1:1.7、1:1.9、1:2.1、1:2.3、1:2.5、1:2.7（每10m高设置一级马道，马道宽2m）。
7. 土方工作高度计算：
平整区土方工作高度 = (地势设计高程 - 货运站地结结构层厚度) - (原地面高程 - 耕植土厚度 - 原地面压实沉降量)
边坡区土方工作高度 = 地势设计高程 - 原地面高程
8. 根据勘察资料，耕植土厚度为0.54m；原地面压实沉降量：按0.03米计。

云南机场集团西南设计研究院有限公司		
资质证书等级：综合甲级		
设计单位：云南机场集团有限责任公司		
设计项目名称：大理机场三期改扩建项目（飞行区及附属配套工程）		
工程名称：飞行区总图工程		
项目负责人	姓名	签字
审核人	陈婷	陈婷
审核人	邵家平	邵家平
专业负责人	邵家平	邵家平
校对人	李一铭	李一铭
检查人	田佩汐	田佩汐
绘图人：XXX		
货站及平滑边坡填筑土方计算图		
设计号	2023-0203	
图号	总施-01变更	
版本号	01	
专业	总图	
比例	1:1000	
日期	2026年1月	