



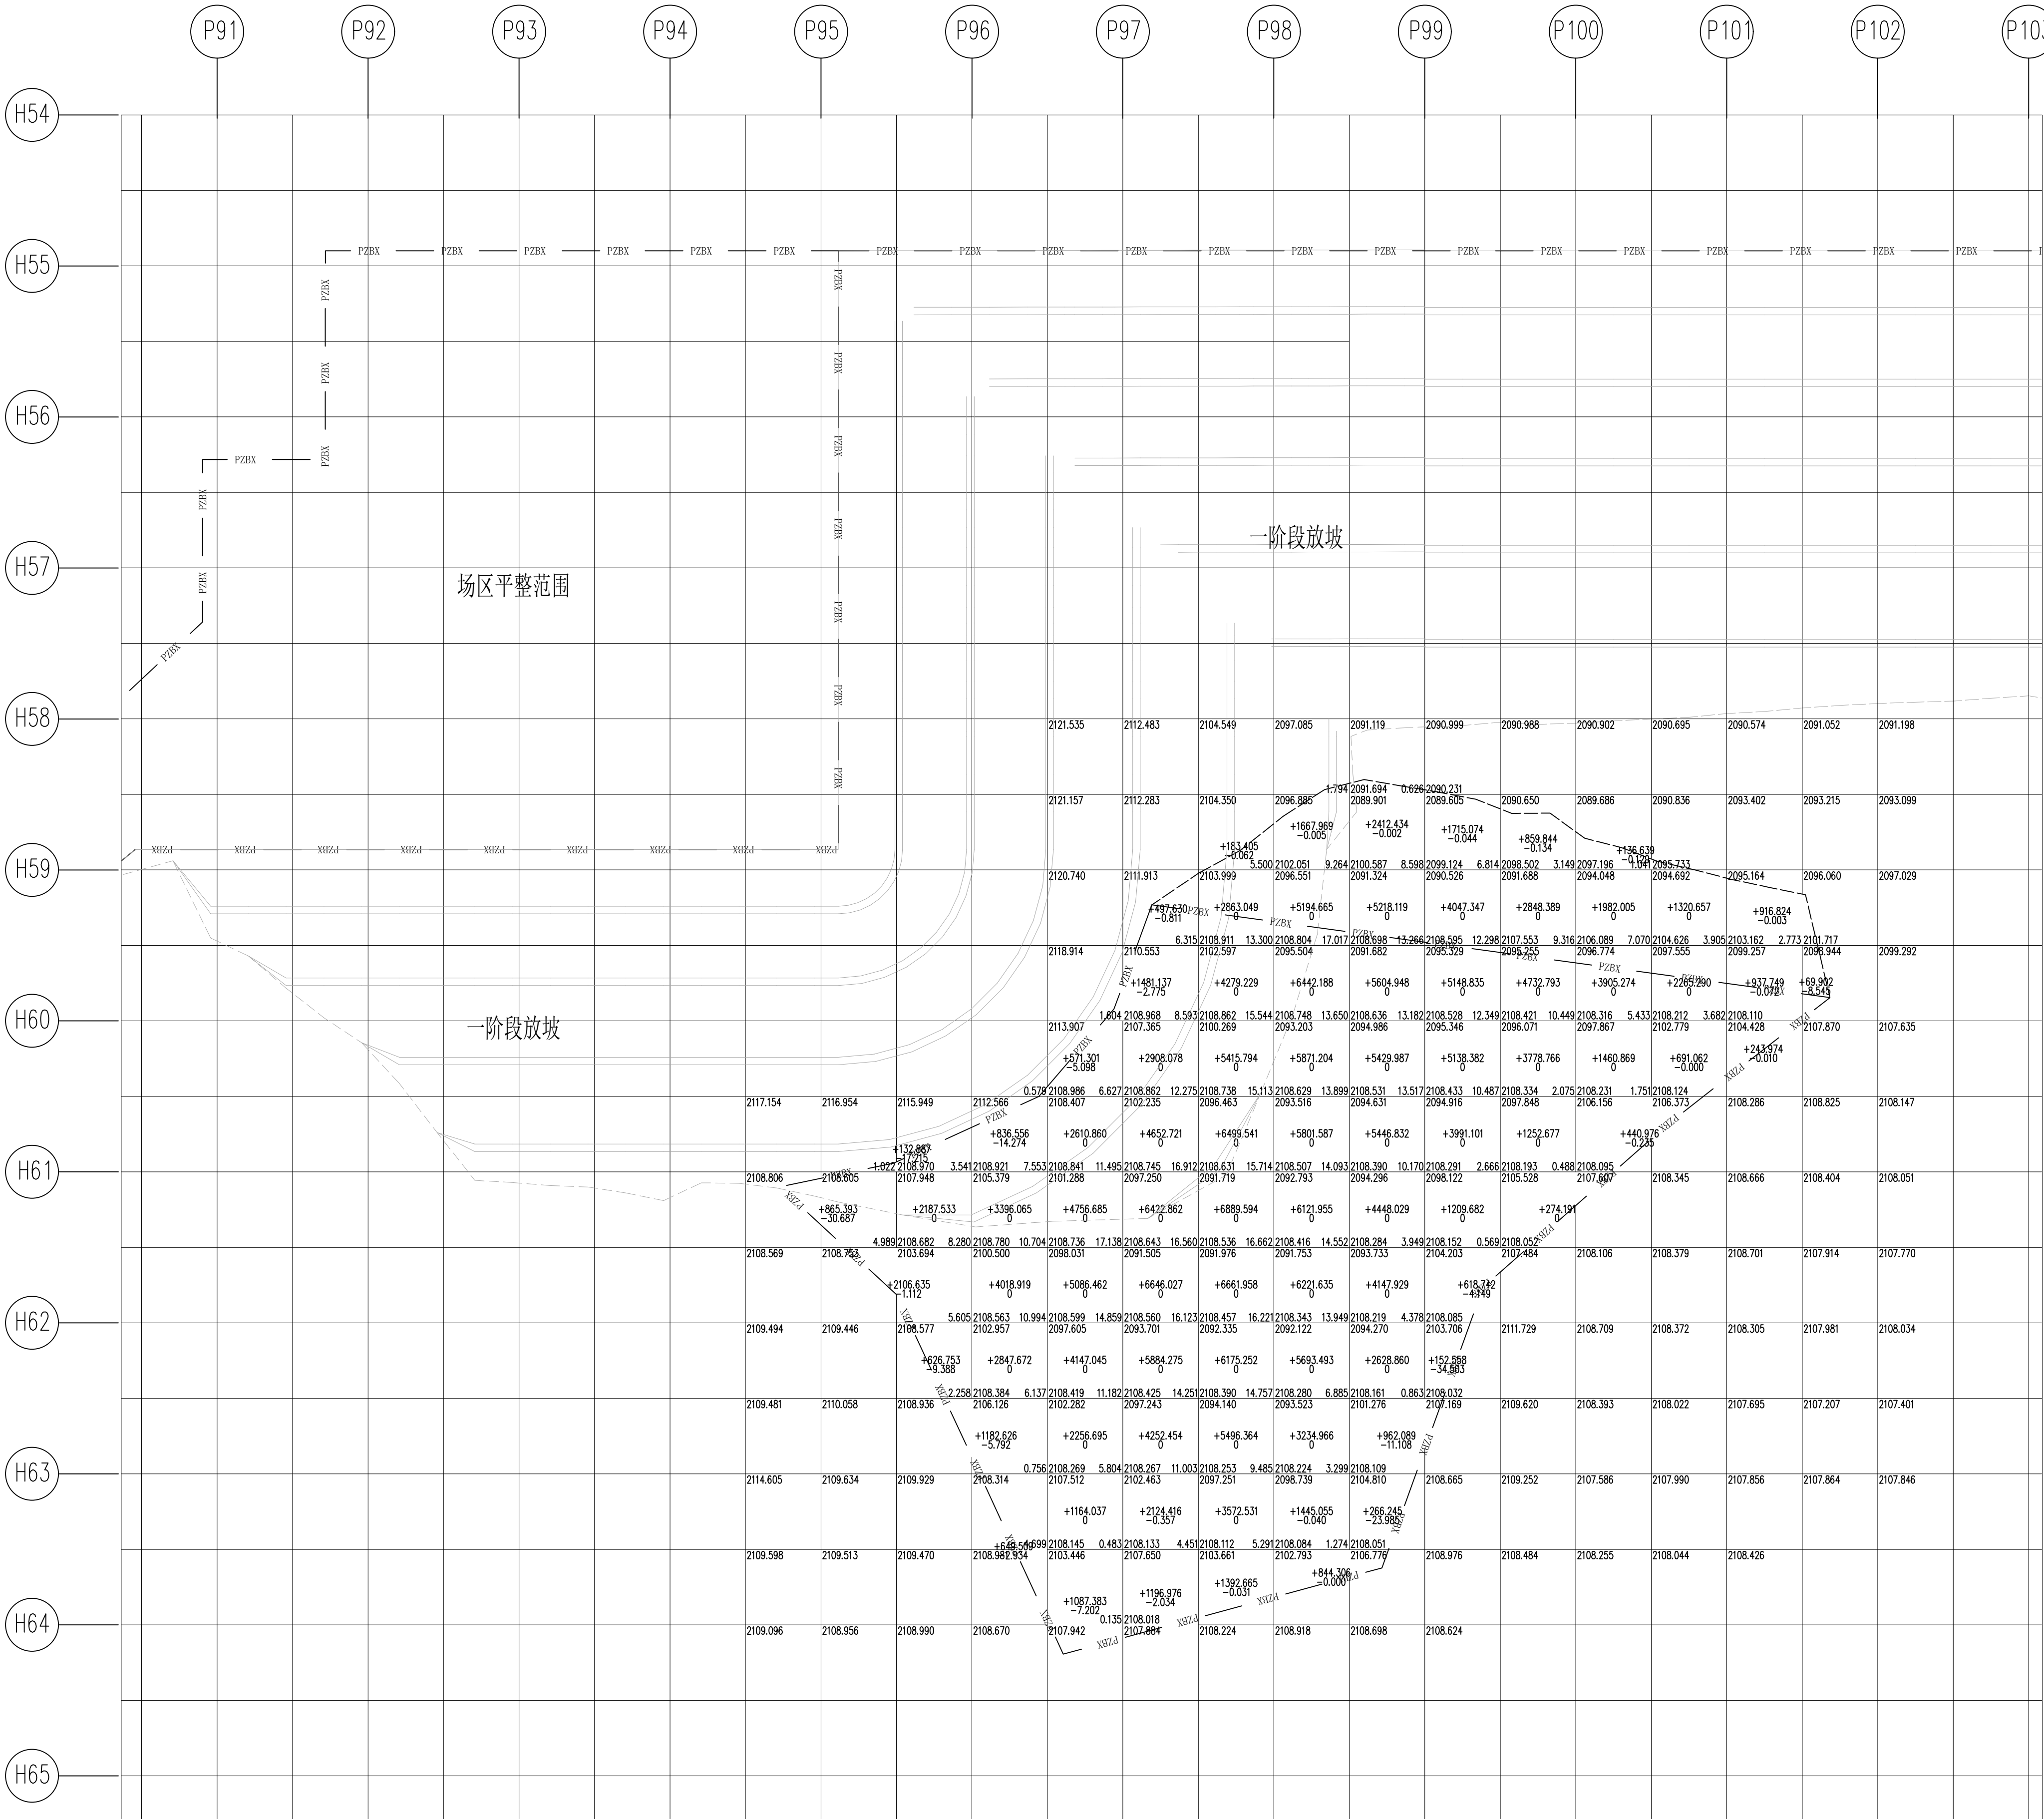

反压平台填筑（铁路弃渣回填）

图例：

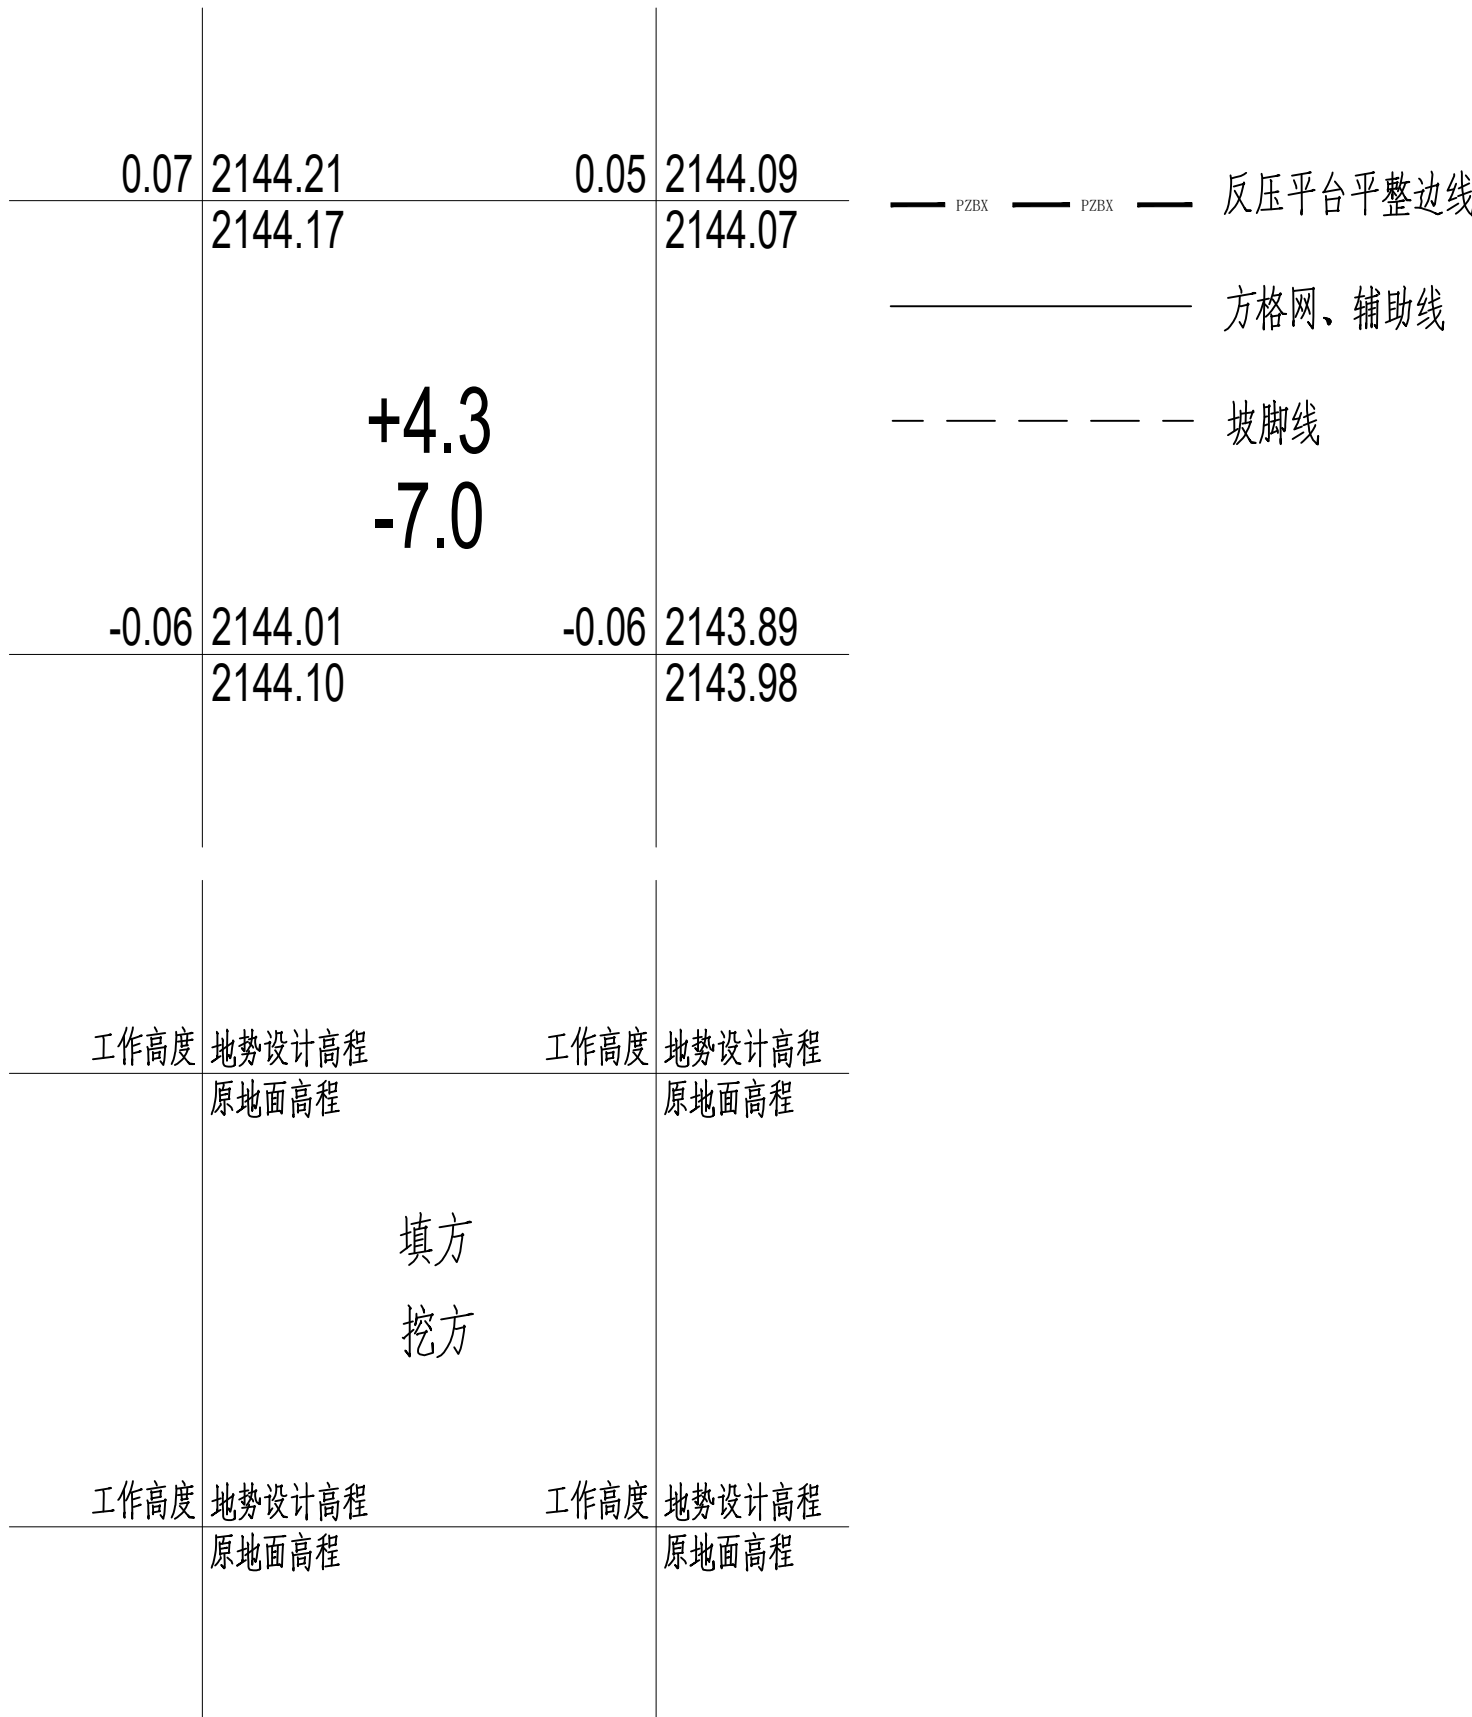

土方量统计表

序号	项目	合计
1	总填方量	261272
2	总挖方量	183

说明：

- 本图使用的地形图包含两部分：机场现状国界范围内及临近区域由中国建筑西南勘察设计研究院有限公司2023年10月提供的测量文件，水塘周边区域根据2025年8月提供的测量文件，尺寸单位以米计。
- 本图采用机场现有40X40米独立方格网，现跑道南端中点桩号为 P50 /H50。垂直跑道方向为 H 坐标，向东递增，平行跑道方向为 P 坐标，向北递增。
- 本图中所注高程采用1985年国家高程基准高程。
- 本次反压平台与现状相接部分，施工时应根据现场实际情况顺接。
- 土方量采用DTM法进行计算，土方压实标准及范围见地基处理相关要求。
- 本图所示的土方计算图为该区域反压平台填筑及放坡，填料采用铁路弃渣。反压平台填方坡比为1:2（每隔10m高设置一级马道，马道宽2m）。
- 土方工作高度计算：
土方工作高度 = 地势设计高程 - 原地面高程

设计单位

DESIGN ORGANIZATION

民航机场建设集团西南设计研究院有限公司

CICC SOUTHWEST DESIGN AND RESEARCH INSTITUTE CO., LTD

建设单位

CLIENT

云南机场集团有限责任公司

项目名称

PROJECT TITLE

大理机场三期改扩建项目（飞行区及附属配套工程）

工程名称

ITEM TITLE

飞行区总图工程

职 责	姓 名	签 字
FUNCTION	NAME	SIGNATURE
审定人	陈婷	
APPROVED BY	陈婷	
审核人	邵家平	
REVIEWED BY	邵家平	
专业负责人	邵家平	
PROFESSIONAL CHIEF	邵家平	
校核人	李一铭	
CHECKED BY	李一铭	
设计人	田佩沙	
DESIGNED BY	田佩沙	

图名

DRAWING TITLE

货运站及平滑反压平台土方计算图

设计号	2023-0203
PROJECT NO.	2023-0203
图号	总施-02（变更）
DRAWING NO.	总施-02（变更）
版本号	01
VERSION	01
专业	总图
DISCIPLINE	总图
比例	1:1000
SCALE	1:1000
日期	2026年1月
DATE	2026年1月