


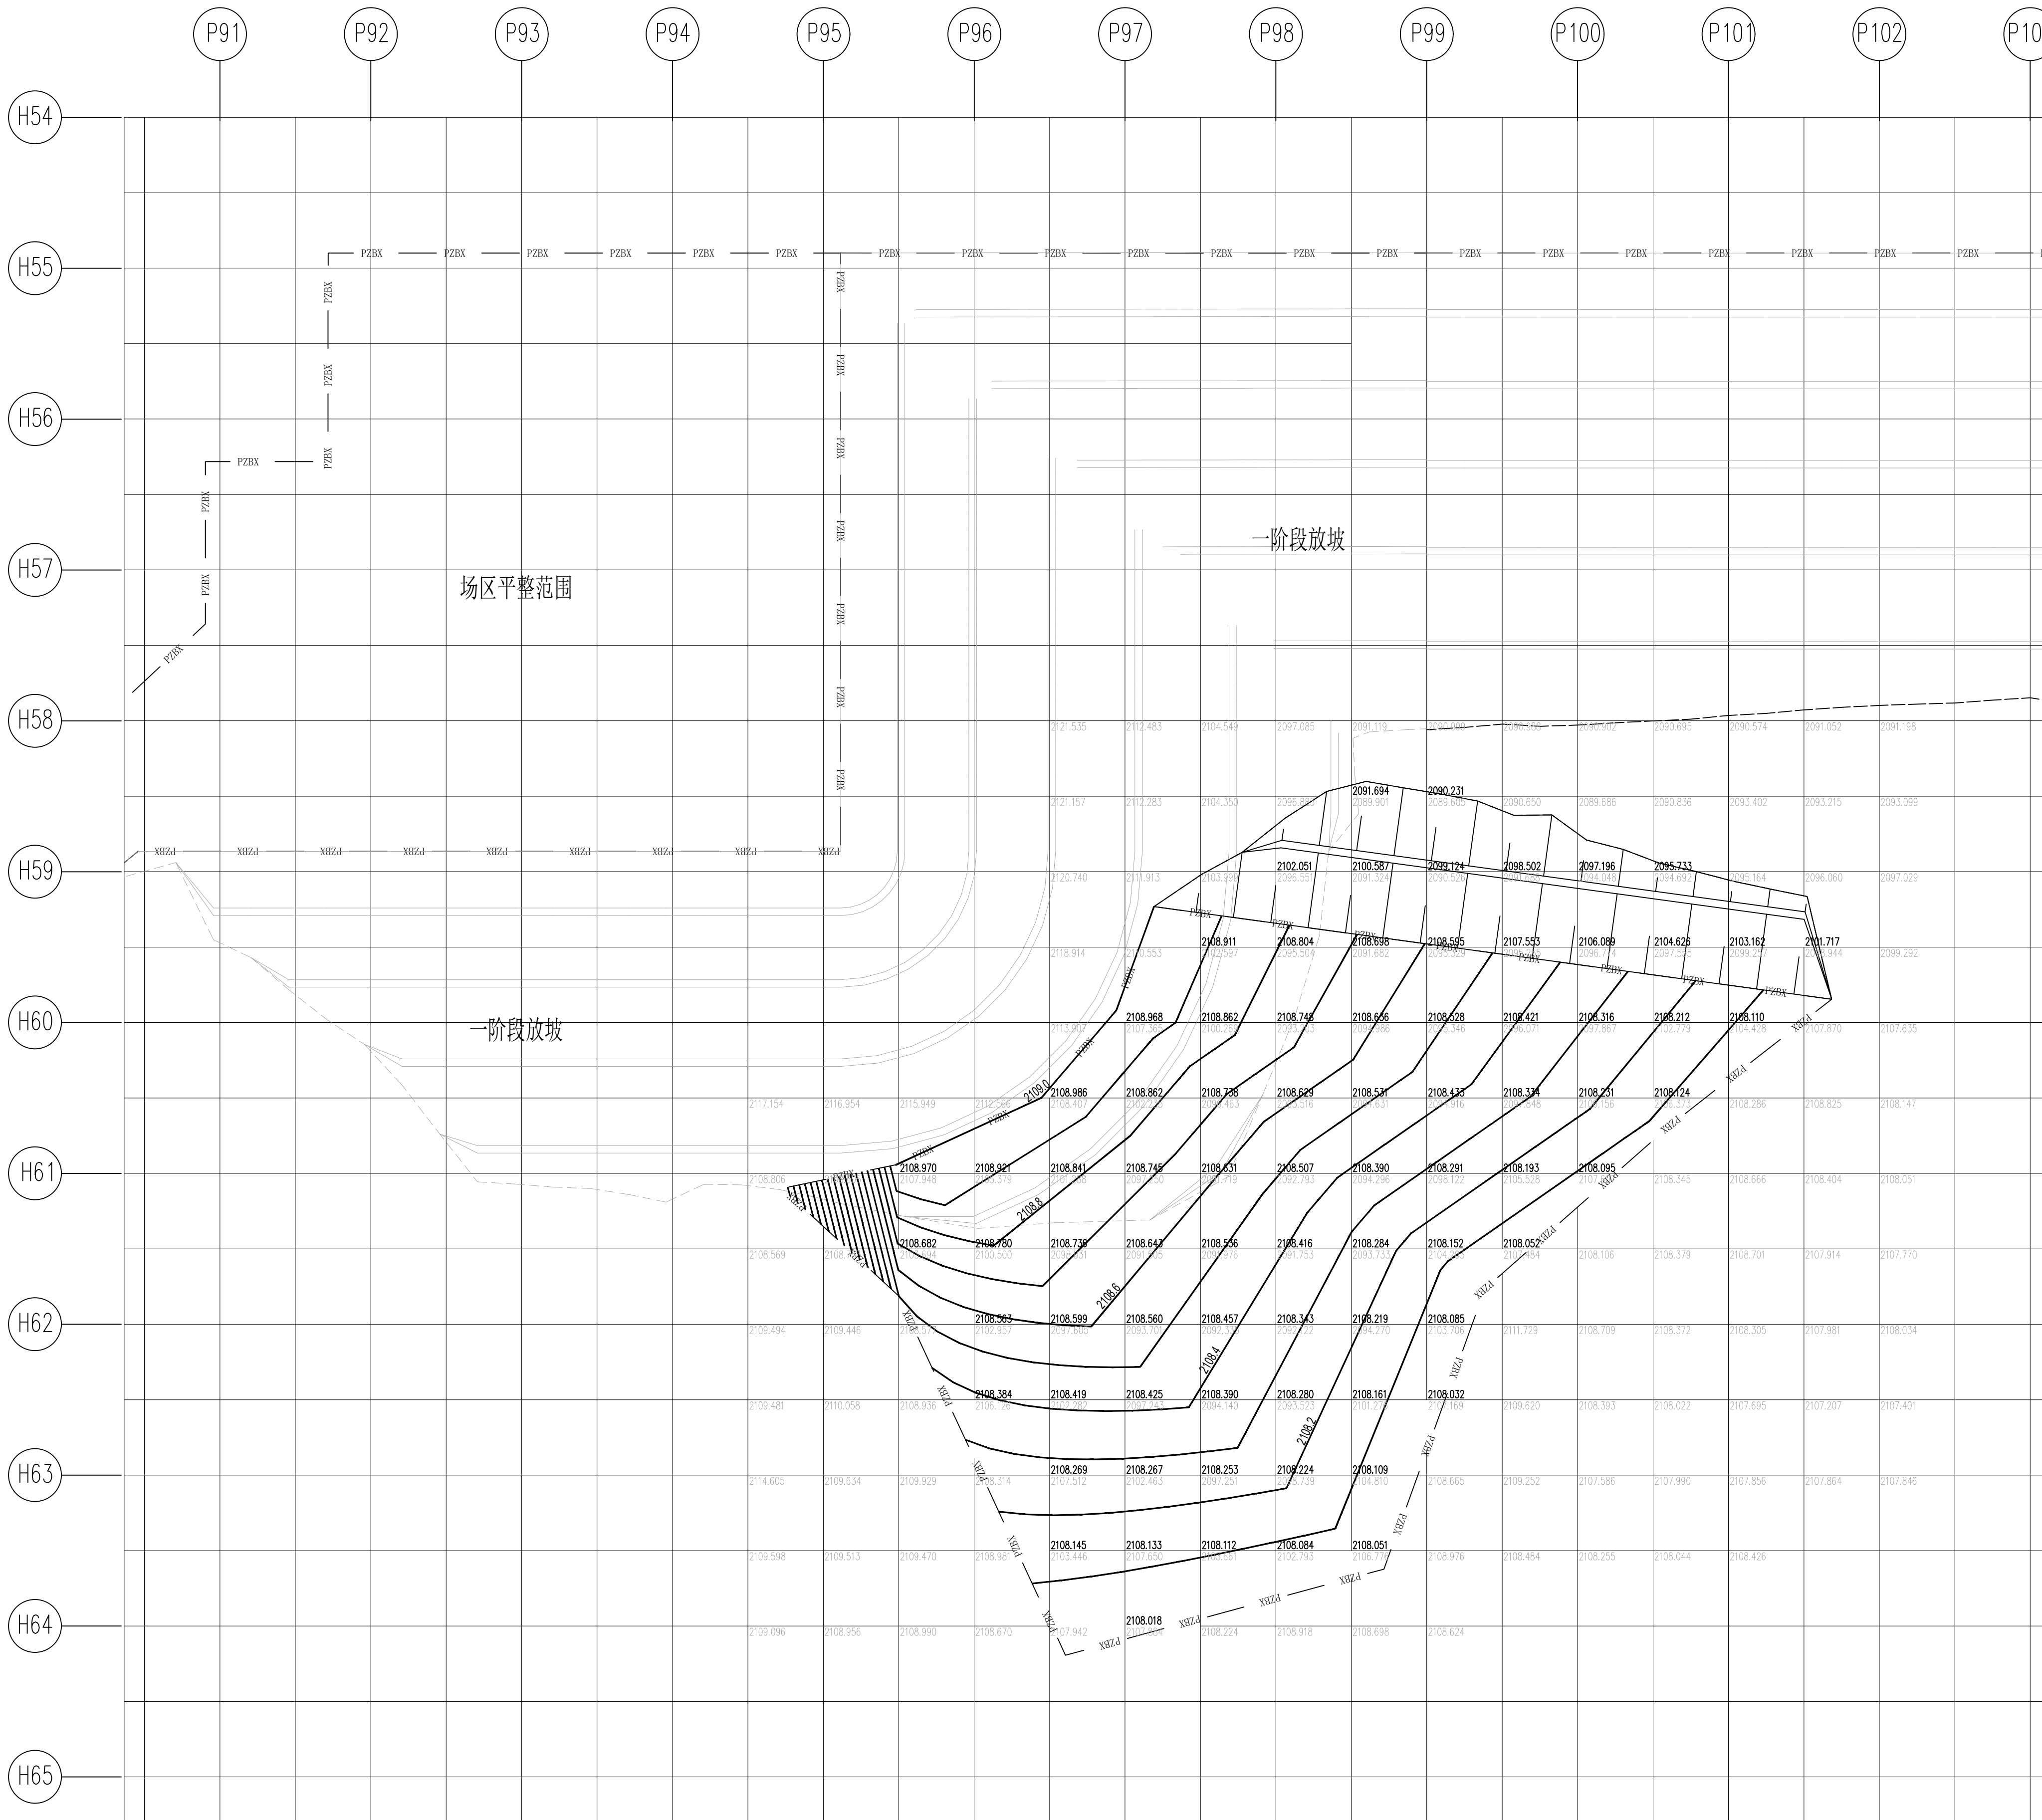

图例：

2144.21	2144.09
2144.17	2144.07
2144.01	2143.89
2144.10	2143.98
地势设计高程	地势设计高程
原地面高程	原地面高程
地势设计高程	地势设计高程
原地面高程	原地面高程

- F25K —— F25K —— 本期用地平整边线
————— 方格网、辅助线
2153.00 地势设计等高线
—— ———— 坡脚线

说明：

1. 本图使用的地形图包含两部分：机场现状围界范围内及临近区域由中国建筑西南勘察设计研究院有限公司2023年10月提供的测量文件，水塘周边区域根据2025年8月提供的测量文件，尺寸单位以米计。
2. 本图采用机场现有40X40米独立方格网，现跑道南端中点桩号为 P50/H50。垂直跑道方向为 H 坐标，向东递增，平行跑道方向为 P 坐标，向北递增。
3. 本图中所注高程采用1985年国家高程基准高程。
4. 本次反压平台与现状相接部分，施工时应根据现场实际情况顺接。
5. 本图设计等高线等高距为0.1米。
6. 本图所示的地势设计图为该区域反压平台填筑及放坡，填料采用铁路弃渣。反压平台填方坡比为1:2（每隔10m高设置一级马道，马道宽2m）。

设计单位 DESIGN ORGANIZATION		
 民航机场建设集团西南设计研究院有限公司 CACI SOUTHWEST DESIGN AND RESEARCH INSTITUTE CO., LTD.		
建设单位 CLIENT		
云南机场集团有限责任公司		
项目名称 PROJECT TITLE		
大理机场三期改扩建项目 (飞行区及附属配套工程)		
工程名称 ITEM TITLE		
飞行区总图工程		
职 责 FUNCTION	姓 名 NAME	签 字 SIGNATURE
审定人 APPROVED BY	陈婷	陈婷
审核人 REVIEWED BY	邵家平	邵家平
专业负责人 SPECIALIST CHIEF	邵家平	邵家平
校核人 CHECKED BY	李一铭	李一铭
设计人 DESIGNED BY	田微汐	田微汐
图 名 DRAWING TITLE		
货运站及平滑 反压平台地势设计图		
设计号 PROJECT NO.	2023-0203	
图号 DRAWING NO.	总施-04（变更）	
版本号 VERSION	01	
专业 FUNCTION	总图	
比例 SCALE	1:1000	
日期 DATE	2026年1月	